인천광역시경제자유구역청 고시 제2019-21호

인천경제자유구역 송도국제도시 지식정보산업단지 실시계획(변경) 승인 및 지형도면 고시

인천광역시경제자유구역청 고시 제2018-35호(2018. 9.17.)로 고시된 송도국제도시 지식정보산업단지 실시계획을 「산업입지 및 개발에 관한 법률」 제18조 및 「경제자유구역의 지정 및 운영에 관한 특별법」 제10조 및 같은 법 시행령 제12조에 따라 실시계획(변경) 고시하고, 「토지이용규제 기본법」 제8조 및 같은 법 시행령 제7조에 따라 지형도면을 고시합니다.

2019년 5월 7일

인천광역시경제자유구역청장

◈ 변경사유

○ 공유재산 매각조건(학교 과밀 해소를 위해 업무시설 중 오피스텔을 건축연면적의 30% 이하로 제한) 및 토지분할 현황을 반영한 지식기반산업지원상업용지(Sd-3, 4) 지구단위계획(가구 및 획지 계획, 건축물에 관한계획, 기타사항에 관한계획 등) 변경

○ 투자유치 시 체결된 토지공급 협약 내용 반영을 위한 지식기반서비스용지(Ia-7) 지구단위계획(건축물의 용도 등) 변경

○ 토지 분할에 따른 Sd-3(9) 차량진출입 허용구간 변경

○ 테크노파크 부문 관련기업용지, R&D용지, 교육시설용지의 지정용도 관계 법률 개정내용(규제방식 변경:포지티브→네거티브)반영 등

◈ 「경제자유구역의 지정 및 운영에 관한 특별법」 제10조 및 같은 법 시행령 제12조 각 호의 사항

1. 단위개발 사업지구의 명칭과 개발사업 시행자의 성명: 변경 없음

2. 개발사업의 목적과 개요: 변경 없음

가. 목 적

나. 토지이용에 관한 계획

구분		면적(㎡)	구성비(%)	비고
합계		2,401,744.7	100.0	
주택건설용지	소계	273,085.1	11.4	
	공동주택	263,967.5	11.0	
	근린생활시설	9,117.6	0.4	
상업업무용지	소계	166,532.0	6.9	
	주상복합	12,958.0	0.5	
	일반상업	69,496.8	2.8	
	지식기반산업지원상업	84,077.2	3.6	
산업시설용지	소계	801,756.1	33.4	
	지식기반서비스	94,525.6	3.9	
	지식기반R&D	18,476.2	0.8	
	지식기반제조업	376,190.8	15.7	
	테크노파크시설	312,563.5	13.0	
공공시설용지	소계	1,160,371.5	48.3	
	교육시설	102,525.7	4.3	
	공공업무	4,000.1	0.2	
	공원	195,127.0	7.9	
	녹지	173,694.3	7.2	
	공공공지	7,112.3	0.3	
	광장	981.4	0.1	
	공공주차장	29,634.2	1.2	
	체육시설	20,771.3	0.8	
	폐기물처리시설	1,600.0	0.1	
	도로	624,925.2	26.2	

※ 인천광역시경제자유구역청 고시 제2018-35호(2018. 9. 17.)

3. 단위개발 사업지구의 위치와 면적: 변경 없음

4. 개발사업 시행기간: 변경 없음

5. 수용이나 사용할 토지 등의 세목: 변경 없음

6. 「국토의 계획 및 이용에 관한 법률」 제30조에 따른 도시관리계획 결정에 관한 사항: 변경 없음

7. 「국토의 계획 및 이용에 관한 법률」 제52조에 따라 작성된 지구단위계획에 관한 사항: 변경 <붙임1>

8. 「산업입지 및 개발에 관한 법률」 제21조 및 「경제자유구역의 지정 및 운영에 관한 특별법」 제11조에 따라 의제되는 허가 등이 있는 경우에는 그 내용: 변경 없음

9. 관련 도서의 열람방법

가. 「산업입지 및 개발에 관한 법률」제19조의2, 「경제자유구역의 지정 및 운영에 관한 특별법」 제10조제2항 및 「국토의 계획 및 이용에 관한 법률」제30조에 따른 관련 도서는 인천경제자유구역청 (개발계획총괄과, ☎ 032-453-7822) 에 갖추어 놓음

나. 지형도면은 「토지이용규제 기본법」 제8조 및 같은 법 시행령 제7조에 따라 토지이용규제시스템(http://luris.molit.go.kr)에서 열람 가능

다. 지형도면 고시는 「경제자유구역의 지정 및 운영에 관한 특별법」 제11조제1항제16호 및 「국토의 계획 및 이용에 관한 법률」 제32조제5항에 따라 도시관리계획 결정(변경) 도서로 갈음

<붙임1> 「국토의 계획 및 이용에 관한 법률」 제52조에 따라 작성된 지구단위계획에 관한 사항: 변경

1 지구단위계획결정(변경)

가. 기반시설의 배치와 규모에 관한 도시관리계획 결정(변경없음)

나. 가구 및 획지의 규모와 조성에 관한 결정(변경)조서

1) 테크노밸리 부문(변경)

도면번호	가구번호	면적(㎡)	획지				비 고
			위치		면적(㎡)		
			기정	변경	기정	변경	
	A-1	96,696.4	-	-	-	-	
	A-2	76,777.1	-	-	-	-	
	A-3	43,105.4	-	-	-	-	
	A-4	47,388.6	-	-	-	-	
	C-1	2,880.4	1	1	586.1	586.1	공동건축(권장)
			2	2	969.1	969.1	공동건축(권장)
			3	3	1,325.2	1,325.2	공동건축(권장)
	C-2	6,237.2	1	1	884.8	884.8	
			2	2	750.2	750.2	공동건축(권장)
			3	3	750.1	750.1	공동건축(권장)
			4	4	733.9	733.9	공동건축(권장)
			5	5	884.8	884.8	
			6	6	749.8	749.8	공동건축(권장)
			7	7	749.8	749.8	공동건축(권장)
			8	8	733.8	733.8	공동건축(권장)
	M-1	12,958.0	1	1	12,958.0	12,958.0	획지분할가능
	Sc-1	59,327.5	1	1	59,327.5	59,327.5	
	Sc-2	10,169.0	1	1	10,169.0	10,169.0	
	Sd-3	14,818.2	3	1	12,137.5	2,483.2	
			-	2		2,469.2	
			-	3		1,090.9	
			-	4		1,239.5	
			-	5		2,431.3	
			-	6		2,423.4	
			9	7	2,680.7	1,439.1	
			-	9		1,241.6	
	Sd-4	9,964.9	3	1	9,964.9	4,982.5	
			-	2		4,982.4	
	Sd-5	36,321.2	1	1	19,465.4	19,465.4	획지분할가능
			2	2	16,855.8	16,855.8	획지분할가능
	Sd-6	9,916.7	1	1	4,957.5	4,957.5	획지분할가능
			4	4	4,959.2	4,959.2	획지분할가능

도면번호	가구번호	면적(㎡)	획지				비 고
			위치		면적(㎡)		
			기정	변경	기정	변경	
	Sd-7	13,056.2	1	1	6,768.8	6,768.8	획지분할가능
			7	7	6,287.4	6,287.4	획지분할가능
	Ia-4	17,475.5	1	1	2,566.0	2,566.0	공동건축(권장)
			2	2	1,985.1	1,985.1	공동건축(권장)
			3	3	2,004.1	2,004.1	공동건축(권장)
			4	4	2,165.0	2,165.0	공동건축(권장)
			5	5	1,777.1	1,777.1	공동건축(권장)
			6	6	2,014.1	2,014.1	공동건축(권장)
			7	7	2,006.1	2,006.1	공동건축(권장)
			8	8	2,958.0	2,958.0	공동건축(권장)
	Ia-5	14,457.6	1	1	3,376.1	3,376.1	공동건축(권장)
			2	2	2,419.1	2,419.1	공동건축(권장)
			3	3	2,411.1	2,411.1	공동건축(권장)
			4	4	2,005.1	2,005.1	공동건축(권장)
			5	5	2,115.1	2,115.1	공동건축(권장)
			6	6	2,131.1	2,131.1	공동건축(권장)
	Ia-6	17,302.3	1	1	3,406.6	3,406.6	획지분할가능
			2	2	7,721.9	7,721.9	획지분할가능
			3	3	6,173.8	6,173.8	
	Ia-7	17,551.5	1	1	5,107.3	5,105.7	
			2	2	12,444.2	9,085.8	획지분할가능
			-	3		3,360.0	
	Ia-9	27,738.7	1	1	12,501.9	12,501.9	획지분할가능
			3	3	15,236.8	15,236.8	획지분할가능
	Ib-2	18,476.2	1	1	5,135.5	5,135.5	공동건축(권장)
			2	2	4,108.6	4,108.6	공동건축(권장)
			3	3	4,631.5	4,631.5	공동건축(권장)
			4	4	4,600.6	4,600.6	공동건축(권장)
	Ic-1	32,780.8	1	1	5,414.0	5,414.0	공동건축(권장)
			2	2	5,444.0	5,444.0	공동건축(권장)
			3	3	6,991.9	6,991.9	공동건축(권장)
			4	4	8,295.9	8,295.9	공동건축(권장)
			5	5	6,635.0	6,635.0	공동건축(권장)

도면 번호	가구 번호	면적(㎡)	획 지				비 고
			위치		면적(㎡)		
			기정	변경	기정	변경	
	Ic-2	92,953.1	1	1	81,275.0	81,275.0	
			2	2	1,977.0	1,977.0	공동건축(권장)
			3	3	1,854.3	1,854.3	공동건축(권장)
			4	4	1,870.4	1,870.4	공동건축(권장)
			5	5	1,886.3	1,886.3	공동건축(권장)
			6	6	2,440.8	2,440.8	공동건축(권장)
			7	7	1,649.3	1,649.3	공동건축(권장)
	Ic-3	4,364.9	1	1	2,241.0	2,241.0	
			2	2	2,123.9	2,123.9	
	Ic-4	5,460.2	1	1	1,672.8	1,672.8	공동건축(권장)
			2	2	1,674.2	1,674.2	공동건축(권장)
			3	3	2,113.2	2,113.2	공동건축(권장)
	Ic-5	17,416.0	1	1	1,718.5	1,718.5	공동건축(권장)
			2	2	2,581.4	2,581.4	공동건축(권장)
			3	3	3,250.4	3,250.4	공동건축(권장)
			4	4	4,787.6	4,787.6	공동건축(권장)
			5	5	5,078.1	5,078.1	공동건축(권장)
	Ic-6	4,941.0	1	1	2,609.0	2,609.0	공동건축(권장)
			2	2	2,332.0	2,332.0	공동건축(권장)
	Ic-7	10,859.9	1	1	10,859.9	10,859.9	
	Ic-8	12,113.8	1	1	3,322.9	3,322.9	공동건축(권장)
			2	2	2,784.0	2,784.0	공동건축(권장)
			3	3	2,787.0	2,787.0	공동건축(권장)
			4	4	3,219.9	3,219.9	공동건축(권장)
	Ic-9	11,279.5	1	1	6,335.3	6,335.3	공동건축(권장) 획지분할가능
			2	2	4,944.2	4,944.2	공동건축(권장)
	Ic-10	19,249.2	1	1	2,553.6	2,553.6	공동건축(권장)
			2	2	1,893.7	1,893.7	공동건축(권장)
			3	3	2,093.7	2,093.7	공동건축(권장)
			4	4	3,564.5	3,564.5	공동건축(권장)
			5	5	1,643.9	1,643.9	공동건축(권장)
			6	6	1,800.7	1,800.7	공동건축(권장)
			7	7	1,963.7	1,963.7	공동건축(권장)
			8	8	1,805.7	1,805.7	공동건축(권장)
			9	9	1,929.7	1,929.7	공동건축(권장)

도면 번호	가구 번호	면적(㎡)	획지				비 고
			위치		면적(㎡)		
			기정	변경	기정	변경	
	Ic-11	11,304.1	1	1	2,003.0	2,003.0	공동건축(권장)
			2	2	1,847.0	1,847.0	공동건축(권장)
			3	3	1,783.0	1,783.0	공동건축(권장)
			4	4	1,705.1	1,705.1	공동건축(권장)
			5	5	1,912.0	1,912.0	공동건축(권장)
			6	6	2,054.0	2,054.0	공동건축(권장)
	Ic-12	15,544.4	1	1	15,544.4	15,544.4	
	Ic-13	25,946.0	1	1	25,946.0	25,946.0	획지분할가능
	Ic-14	32,017.6	1	1	32,017.6	32,017.6	획지분할가능
	Ic-15	26,526.9	1	1	7,333.0	7,333.0	공동건축(권장)
			2	2	5,503.0	5,503.0	공동건축(권장)
			3	3	6,041.0	6,041.0	공동건축(권장)
			4	4	7,649.9	7,649.9	공동건축(권장)
	Ic-16	26,182.5	1	1	26,182.5	26,182.5	획지분할가능
	Ic-17	7,723.8	1	1	7,723.8	7,723.8	획지분할가능
	Ic-18	10,827.0	1	1	5,413.5	5,413.5	획지분할가능
			3	3	5,413.5	5,413.5	획지분할가능
	Ic-19	8,700.1	1	1	8,700.1	8,700.1	획지분할가능
	Po-1	4,000.1	1	1	1,322.0	1,322.0	
			2	2	2,678.1	2,678.1	획지분할가능

※ 본 조서상의 획지면적과 공부상의 면적이 상이할 경우 공부상의 면적을 우선함

▨ 가구 및 획지의 조성에 관한 결정 변경 사유서

가구번호	면적(㎡)	획지				변경사유
		위치		면적(㎡)		
		기정	변경	기정	변경	
Sd-3	14,818.2	3	1	12,137.5	2,483.2	○공유재산 매각을 위한 토지분할 결과반영
		-	2		2,469.2	
		-	3		1,090.9	
		-	4		1,239.5	
		-	5		2,431.3	
		-	6		2,423.4	
		9	7	2,680.7	1,439.1	
		-	9		1,241.6	
Sd-4	9,964.9	3	1	9,964.9	4,982.5	
		-	2		4,982.4	
Ia-7	17,551.5	1	1	5,107.3	5,105.7	○투자유치를 위한 토지분할 결과반영
		2	2	12,444.2	9,085.8	
		-	3		3,360.0	

2) 테크노파크 부문(변경없음)

3) 공공시설용지 부문(변경없음)

다. 건축물의 용도・건폐율・용적률・높이・배치・형태・색채・건축선에 관한 도시관리계획 결정조서(변경)

1) 테크노밸리 부문(변경)

(1) 공동주택용지(변경없음)

(2) 근린생활시설용지(변경없음)

(3) 주상복합용지(변경없음)

(4) 일반상업용지(변경없음)

(5) 지식기반산업지원상업용지(변경)

▨ 간선가로변 (Sd-3(9), Sd-4, Sd-5, Sd-7(7)) → (Sd-3(7), Sd-5, Sd-7(7))

도면번호	위치	구분		계 획 내 용
	<기정> Sd-3(9) Sd-4 Sd-5 Sd-7(7)	용도	기정	○ 지정용도 - 제1종근린생활시설 - 제2종근린생활시설(‘라’목 중 옥외골프연습장, ‘차’목 및 ‘타’목 중 안마시술소 제외) - 문화 및 집회시설 중 ‘가’목 및 ‘라’목 - 판매시설 - 의료시설 중 ‘가’목 (정신병원 및 요양병원 제외) - 교육연구시설 중 ‘라’목 - 운동시설 중 ‘가’목 (옥외골프연습장 제외) - 업무시설 - 위험물저장 및 처리시설(주유소 및 석유판매소) - 자동차관련시설 중 ‘가’목 - 방송통신시설 - 관광휴게시설 중 ‘가’목, ‘나’목, ‘다’목 ○ 불허용도 - 권장용도 이외의 용도
	<변경> Sd-3(7) Sd-5 Sd-7(7)		변경	○ 지정용도 - 제1종근린생활시설 - 제2종근린생활시설(‘라’목 중 옥외골프연습장, ‘차’목 및 ‘타’목 중 안마시술소 제외) - 문화 및 집회시설 중 ‘가’목 및 ‘라’목 - 판매시설 - 의료시설 중 ‘가’목 (정신병원 및 요양병원 제외) - 교육연구시설 중 ‘라’목 - 운동시설 중 ‘가’목 (옥외골프연습장 제외) - 업무시설 - 위험물저장 및 처리시설(주유소 및 석유판매소) - 자동차관련시설 중 ‘가’목 - 방송통신시설 - 관광휴게시설 중 ‘가’목, ‘나’목, ‘다’목 ○ 불허용도 - 지정용도 이외의 용도

도면번호	위치	구분		계 획 내 용
	<기정> Sd-3(9) Sd-4 Sd-5 Sd-7(7) <변경> Sd-3(7) Sd-5 Sd-7(7)	건폐율		○50%이하
		용적률	기정	○Sd-5(2) : 250%이하 ○Sd-3(9), Sd-4, Sd-5(1), Sd-7(7) : 350%이하
			변경	○Sd-5(2) : 250%이하 ○Sd-3(7), Sd-5(1), Sd-7(7) : 350%이하
		높이		- 건축허가 이전에 인천경제자유구역청 경관위원회자문(심의)를 통해서 결정
		배치		○건축물의 벽면은 도로(보행자전용도로 제외)변과 평행 ○보행자전용 도로변에 면한 건축물은 보행자전용 도로변으로부터 보행자의 진출입이 가능하도록 할 것(권장) ○획지분할가능 및 공동건축에 대하여는 지구단위계획결정도 참조 ○획지분할시 공동건축은 적용하지 아니함
		형태		○저층부(1층)는 투시형 벽면이나 투시형 셔터 사용 - 투시형 벽면 : 도로에 접한 벽면에 한하여 벽면적의 50%이상 투시벽으로 처리 - 투시형 셔터 : 셔터를 설치할 경우 투시형으로 처리 (보행자전용도로에 접하는 부분 포함) ○건축물의 전후면과 측면은 동일계통의 재료, 색채 사용 ○옥상부분은 냉각탑 등 건축설비가 노출되지 않도록 할 것
		색채		○주조색 : 10YR ~ 2.5GY 8.5이상/2이하, N8 이상 ○보조색 : 10YR ~ 2.5GY 6~8/2~4 ○강조색 : 10YR ~ 2.5GY 3~5/4~9
		건축선	기정	○건축지정선 - 광1-2호선변(Sd-4) : 제1호건축선 (9m, 도로후퇴부 6m) ○건축한계선 - 광1-2호선, 대1-36호선변(Sd-1, Sd-4, Sd-5) : 제1호건축선 (9m, 도로후퇴부분 6m) - 대1-26호선변(Sd-7(7)) : 제2호건축선 (6m, 도로후퇴부분 3m) - 대2-62호선, 대1-36호선변(Sd-3(9), Sd-7(7)) : 제2호건축선 (6m 도로후퇴부분 3m) - 10, 15m도로변(Sd-1, Sd-3(9), Sd-4, Sd-7(7)) : 제3호건축선 (3m) - 15m 도로변(Sd-5) : 제2호건축선 (6m 도로후퇴부분 3m)
			변경	○건축한계선 - 광1-2호선, 대1-36호선변(Sd-5) : 제1호건축선 (9m, 도로후퇴부분 6m) - 대1-26호선변(Sd-7(7)) : 제2호건축선 (6m, 도로후퇴부분 3m) - 대2-62호선, 대1-36호선변(Sd-3(7), Sd-7(7)) : 제2호건축선 (6m 도로후퇴부분 3m) - 10, 15m도로변(Sd-3(7), Sd-7(7)) : 제3호건축선 (3m) - 15m 도로변(Sd-5) : 제2호건축선 (6m 도로후퇴부분 3m)

➡ 사유 : 공유재산 토지분할 결과 반영에 따른 획지분할

▨ 간선가로변 (Sd-3(9), Sd-4, Sd-5, Sd-7(7)) → (Sd-3(9), Sd-4(1,2))

도면번호	위치	구분		계 획 내 용
	<기정> Sd-3(9) Sd-4 Sd-5 Sd-7(7) <변경> Sd-3(9) Sd-4(1,2)	용도	기정	○지정용도 - 제1종근린생활시설 - 제2종근린생활시설(‘라’목 중 옥외골프연습장, ‘차’목 및 ‘타’목 중 안마시술소 제외) - 문화 및 집회시설 중 ‘가’목 및 ‘라’목 - 판매시설 - 의료시설 중 ‘가’목 (정신병원 및 요양병원 제외) - 교육연구시설 중 ‘라’목 - 운동시설 중 ‘가’목 (옥외골프연습장 제외) - 업무시설 - 위험물저장 및 처리시설(주유소 및 석유판매소) - 자동차관련시설 중 ‘가’목 - 방송통신시설 - 관광휴게시설 중 ‘가’목, ‘나’목, ‘다’목 ○불허용도 - 권장용도 이외의 용도
			변경	○지정용도 - 제1종근린생활시설 - 제2종근린생활시설(‘라’목 중 옥외골프연습장, ‘차’목 및 ‘타’목 중 안마시술소 제외) - 문화 및 집회시설 중 ‘가’목 및 ‘라’목 - 판매시설 - 의료시설 중 ‘가’목 (정신병원 및 요양병원 제외) - 교육연구시설 중 ‘라’목 - 운동시설 중 ‘가’목 (옥외골프연습장 제외) - 업무시설 (단, 오피스텔은 건축연면적(주차장 및 기계실 등 제외)의 30% 이하로 함) - 위험물저장 및 처리시설(주유소 및 석유판매소) - 자동차관련시설 중 ‘가’목 - 방송통신시설 - 관광휴게시설 중 ‘가’목, ‘나’목, ‘다’목 ○불허용도 - 지정용도 이외의 용도
		건폐율		○50%이하
		용적률	기정	○Sd-5(2) : 250%이하 ○Sd-3(9), Sd-4, Sd-5(1), Sd-7(7) : 350%이하
			변경	○Sd-3(9), Sd-4(1,2) : 350%이하
		높이		○건축허가 이전에 인천경제자유구역청 경관위원회자문(심의)를 통해서 결정

도면번호	위치	구분		계 획 내 용
		배치		○ 건축물의 벽면은 도로(보행자전용도로 제외)변과 평행 ○ 보행자전용 도로변에 면한 건축물은 보행자전용 도로변으로부터 보행자의 진출입이 가능하도록 할 것(권장) ○ 획지분할가능 및 공동건축에 대하여는 지구단위계획결정도 참조 ○ 획지분할시 공동건축은 적용하지 아니함
		형태		○ 저층부(1층)는 투시형 벽면이나 투시형 셔터 사용 - 투시형 벽면 : 도로에 접한 벽면에 한하여 벽면적의 50%이상 투시벽 으로 처리 - 투시형 셔터 : 셔터를 설치할 경우 투시형으로 처리 (보행자전용도로에 접하는 부분 포함) ○ 건축물의 전후면과 측면은 동일계통의 재료, 색채 사용 ○ 옥상부분은 냉각탑 등 건축설비가 노출되지 않도록 할 것
	<기정> Sd-3(9) Sd-4 Sd-5 Sd-7(7) <변경> Sd-3(9) Sd-4(1,2)	색채		○ 주조색 : 10YR ~ 2.5GY 8.5이상/2이하, N8 이상 ○ 보조색 : 10YR ~ 2.5GY 6~8/2~4 ○ 강조색 : 10YR ~ 2.5GY 3~5/4~9
		건축선	기정	○ 건축지정선 - 광1-2호선변(Sd-4) : 제1호건축선 (9m, 도로후퇴부 6m) ○ 건축한계선 - 광1-2호선, 대1-36호선변(Sd-1, Sd-4, Sd-5) : 제1호건축선 (9m, 도로후퇴부분 6m) - 대1-26호선변(Sd-7(7)) : 제2호건축선 (6m, 도로후퇴부분 3m) - 대2-62호선, 대1-36호선변(Sd-3(9), Sd-7(7)) : 제2호건축선 (6m 도로후퇴부분 3m) - 10, 15m도로변(Sd-1, Sd-3(9), Sd-4, Sd-7(7)) : 제3호건축선 (3m) - 15m 도로변(Sd-5) : 제2호건축선 (6m 도로후퇴부분 3m)
			변경	○ 건축지정선 - 광1-2호선변(Sd-4(1,2)) : 제1호건축선 (9m, 도로후퇴부 6m) ○ 건축한계선 - 광1-2호선, 대1-36호선변(Sd-4(1,2)) : 제1호건축선 (9m, 도로후퇴부분 6m) - 대2-62호선, 대1-36호선변(Sd-3(9)) : 제2호건축선 (6m 도로후퇴부분 3m) - 10, 15m도로변(Sd-3(9), Sd-4(1,2)) : 제3호건축선 (3m)

➡ 사유 : 공유재산 매각조건[업무시설(단, 오피스텔은 건축연면적(주차장 및 기계실 등 제외)의 30% 이하로 함)]에 따른 건축물의 용도 변경

▨ 이면가로변 (Sd-3(1, 3), Sd-6, Sd-7(1)) → (Sd-3(3, 4), Sd-6, Sd-7(1))

도면번호	위치	구분		계 획 내 용
	<기정> Sd-3(3) Sd-6 Sd-7(1)	용도	기정	○지정용도 - 제1종근린생활시설 - 제2종근린생활시설 ('라'목 중 옥외골프연습장, '차'목 및 '타'목 중 안마시술소 제외) - 판매시설 - 의료시설 중 '가'목(정신병원 및 요양병원 제외) - 교육연구시설 중 '라'목 - 운동시설 중 '가'목 (옥외골프연습장 제외) - 업무시설 - 자동차관련시설 중 '가'목, '나'목 - 관광휴게시설 중 '가'목, '나'목, '다'목 ○불허용도 - 권장용도 이외의 용도
			변경	○지정용도 - 제1종근린생활시설 - 제2종근린생활시설 ('라'목 중 옥외골프연습장, '차'목 및 '타'목 중 안마시술소 제외) - 판매시설 - 의료시설 중 '가'목(정신병원 및 요양병원 제외) - 교육연구시설 중 '라'목 - 운동시설 중 '가'목 (옥외골프연습장 제외) - 업무시설 - 자동차관련시설 중 '가'목, '나'목 - 관광휴게시설 중 '가'목, '나'목, '다'목 ○불허용도 - 지정용도 이외의 용도
	<변경> Sd-3(3,4) Sd-6 Sd-7(1)	건폐율		○50%이하
		용적률	기정	○Sd-3(3) : 300%이하 ○Sd-6, Sd-7(1) : 350%이하
			변경	○Sd-3(3,4) : 300%이하 ○Sd-6, Sd-7(1) : 350%이하
		높이		○건축허가 이전에 인천경제자유구역청 도시경관자문단의 자문 또는 사전경관 협의를 통해서 결정
		배치		○건축물의 벽면은 도로(보행자전용도로 제외)변과 평행 ○보행자전용 도로변에 면한 건축물은 보행자전용 도로변으로부터 보행자의 진출입이 가능하도록 할 것(권장)
		형태		○저층부(1층)는 투시형 벽면이나 투시형 셔터 사용 - 투시형 벽면 : 도로에 접한 벽면에 한하여 벽면적의 50%이상을 투시벽으로 처리 - 투시형 셔터 : 셔터를 설치할 경우 투시형으로 처리 (보행자전용도로와 접하는 부분 포함) ○건축물의 전후면과 측면은 동일계통의 재료, 색채 사용 ○옥상부분은 냉각탑 등 건축설비가 노출되지 않도록 할 것
		색채		○주조색 : 10YR ~ 2.5GY 8.5이상/2이하, N8 이상 ○보조색 : 10YR ~ 2.5GY 6~8/2~4 ○강조색 : 10YR ~ 2.5GY 3~5/4~9
		건축선		○건축한계선 - 광2-12호선변 : 제1호건축선 (9m, 도로후퇴부 6m) - 대1-26호선, 대2-62호선변 : 제2호건축선 (6m, 도로후퇴부분3m) - 10, 15m 도로변 : 제3호건축선 (3m)

➡ 사유 : 공유재산 토지분할 결과 반영에 따른 획지분할

▨ 이면가로변 (Sd-3(1, 3), Sd-6, Sd-7(1)) → (Sd-3(1, 2, 5, 6))

도면번호	위치	구분		계 획 내 용
	<기정> Sd-3(3) Sd-6 Sd-7(1) <변경> Sd-3 (1,2,5,6)	용도	기정	○지정용도 - 제1종근린생활시설 - 제2종근린생활시설 ('라'목 중 옥외골프연습장, '차'목 및 '타'목 중 안마시술소 제외) - 판매시설 - 의료시설 중 '가'목(정신병원 및 요양병원 제외) - 교육연구시설 중 '라'목 - 운동시설 중 '가'목 (옥외골프연습장 제외) - 업무시설 - 자동차관련시설 중 '가'목, '나'목 - 관광휴게시설 중 '가'목, '나'목, '다'목 ○불허용도 - 권장용도 이외의 용도
			변경	○지정용도 - 제1종근린생활시설 - 제2종근린생활시설 ('라'목 중 옥외골프연습장, '차'목 및 '타'목 중 안마시술소 제외) - 판매시설 - 의료시설 중 '가'목(정신병원 및 요양병원 제외) - 교육연구시설 중 '라'목 - 운동시설 중 '가'목 (옥외골프연습장 제외) - 업무시설 (단, 오피스텔은 건축연면적(주차장 및 기계실 등 제외)의 30% 이하로 함) - 자동차관련시설 중 '가'목, '나'목 - 관광휴게시설 중 '가'목, '나'목, '다'목 ○불허용도 - 지정용도 이외의 용도
		건폐율		○50%이하
		용적률	기정	○Sd-3(3) : 300%이하 ○Sd-6, Sd-7(1) : 350%이하
			변경	○Sd-3(1,2,5,6) : 300%이하
		높이		○건축허가 이전에 인천경제자유구역청 도시경관자문단의 자문 또는 사전경관 협의를 통해서 결정
		배치		○건축물의 벽면은 도로(보행자전용도로 제외)변과 평행 ○보행자전용 도로변에 면한 건축물은 보행자전용 도로변으로부터 보행자의 진출입이 가능하도록 할 것(권장)
		형태		○저층부(1층)는 투시형 벽면이나 투시형 셔터 사용 - 투시형 벽면 : 도로에 접한 벽면에 한하여 벽면적의 50%이상을 투시벽으로 처리 - 투시형 셔터 : 셔터를 설치할 경우 투시형으로 처리 (보행자전용도로와 접하는 부분 포함) ○건축물의 전후면과 측면은 동일계통의 재료, 색채 사용 ○옥상부분은 냉각탑 등 건축설비가 노출되지 않도록 할 것
		색채		○주조색 : 10YR ~ 2.5GY 8.5이상/2이하, N8 이상 ○보조색 : 10YR ~ 2.5GY 6~8/2~4 ○강조색 : 10YR ~ 2.5GY 3~5/4~9
		건축선		○건축한계선 - 광2-12호선변 : 제1호건축선 (9m, 도로후퇴부 6m) - 대1-26호선, 대2-62호선변 : 제2호건축선 (6m, 도로후퇴부분3m) - 10, 15m 도로변 : 제3호건축선 (3m)

➡ 사유 : 공유재산 매각조건[업무시설(단, 오피스텔은 건축연면적(주차장 및 기계실 등 제외)의 30% 이하로 함)]에 따른 건축물의 용도 변경

(6) 지식기반서비스용지(변경)

도면번호	위치	구분		계 획 내 용
	Ia-7	용도	기정	► Ia-7(1) ○ 지정용도 - 주용도 : 연면적(주차장 및 기계실 등 제외)의 50% 이상 • 업무시설(오피스텔 제외) - 부용도 : 연면적(주차장 및 기계실 등 제외)의 50% 이하 (단, 오피스텔 30%이하, 오피스텔 이외의 부용도 40%이하) • 제1종근린생활시설 (‘가’목, ‘나’목, ‘다’목, ‘라’목에 한하며, ‘라’목 중 안마원 제외) • 제2종근린생활시설 (‘나’목 종교집회장, ‘마’목 총포판매소, ‘차’목 중 장의사, ‘파’목 중 옥외골프연습장, ‘거’목 다중생활시설, ‘더’목 단란주점, ‘러’목 안마시술소, 노래연습장 제외) • 문화 및 집회시설(‘라’목 전시장) • 교육연구시설(‘라’목 학원, ‘마’목 연구소) • 업무시설(오피스텔에 한함) ○ 불허용도 - 지정용도 이외의 용도 ► Ia-7(2) ○ 지정용도 - 주용도 : 연면적(주차장 및 기계실 등 제외)의 80% 이상 • 업무시설 (오피스텔 제외) - 부용도 : 연면적(주차장 및 기계실 등 제외)의 20% 이하 • 제1종근린생활시설 (‘가’목, ‘나’목, ‘다’목, ‘라’목에 한하며, ‘라’목 중 안마원 제외) • 제2종근린생활시설 (‘나’목 종교집회장, ‘마’목 총포판매소, ‘차’목 중 장의사, ‘파’목 중 옥외골프연습장, ‘거’목 다중생활시설, ‘더’목 단란주점, ‘러’목 안마시술소, 노래연습장 제외) • 문화 및 집회시설(‘라’목 전시장) • 교육연구시설(‘라’목 학원, ‘마’목 연구소) ○ 불허용도 - 지정용도 이외의 용도

도면 번호	위치	구분		계 획 내 용
	Ia-7	용도	변경	▶ Ia-7(1) ○ 지정용도 - 주용도 : 연면적(주차장 및 기계실 등 제외)의 50% 이상 • 업무시설(오피스텔 제외) - 부용도 : 연면적(주차장 및 기계실 등 제외)의 50% 이하 (단, 오피스텔 30%이하, 오피스텔 이외의 부용도 40%이하) • 제1종근린생활시설 (‘가’목, ‘나’목, ‘다’목, ‘라’목에 한하며, ‘라’목 중 안마원 제외) • 제2종근린생활시설 (‘나’목 종교집회장, ‘마’목 총포판매소, ‘차’목 중 장의사, ‘파’목 중 옥외 골프연습장, ‘거’목 다중생활시설, ‘더’목 단란주점, ‘러’목 안마시술소, 노래연습장 제외) • 문화 및 집회시설(‘라’목 전시장) • 교육연구시설(‘라’목 학원, ‘마’목 연구소) • 업무시설(오피스텔에 한함) ○ 불허용도 - 지정용도 이외의 용도 ▶ Ia-7(2) ○ 지정용도 - 주용도 : 연면적(주차장 및 기계실 등 제외)의 80% 이상 • 업무시설 (오피스텔 제외) - 부용도 : 연면적(주차장 및 기계실 등 제외)의 20% 이하 • 제1종근린생활시설 (‘가’목, ‘나’목, ‘다’목, ‘라’목에 한하며, ‘라’목 중 안마원 제외) • 제2종근린생활시설 (‘나’목 종교집회장, ‘마’목 총포판매소, ‘차’목 중 장의사, ‘파’목 중 옥외 골프연습장, ‘거’목 다중생활시설, ‘더’목 단란주점, ‘러’목 안마시술소, 노래연습장 제외) • 문화 및 집회시설(‘라’목 전시장) • 교육연구시설(‘라’목 학원, ‘마’목 연구소) ○ 불허용도 - 지정용도 이외의 용도 ▶ Ia-7(3) ○ 지정용도 - 주용도 : 연면적(주차장 및 기계실 등 제외)의 80% 이상 • 업무시설 (오피스텔 제외) • 문화 및 집회시설(‘라’목 전시장) • 교육연구시설(‘나’목 교육원, ‘다’목 직업훈련소, ‘마’목 연구소) - 부용도 : 연면적(주차장 및 기계실 등 제외)의 20% 이하 • 제1종근린생활시설 (‘가’목, ‘나’목, ‘다’목, ‘라’목에 한하며, ‘라’목 중 안마원 제외) • 제2종근린생활시설 (‘나’목 종교집회장, ‘마’목 총포판매소, ‘차’목 중 장의사, ‘파’목 중 옥외 골프연습장, ‘거’목 다중생활시설, ‘더’목 단란주점, ‘러’목 안마시술소, 노래연습장 제외) ○ 불허용도 - 지정용도 이외의 용도

도면 번호	위치	구분	계 획 내 용
	Ia-7	건폐율	○ 50%이하
		용적률	○ 300%이하
		높이	○ 건축허가 이전에 인천경제자유구역청 경관위원회(심의)를 통해서 결정
		배치	○ 건축물의 벽면은 도로(보행자전용도로 제외)변과 평행 ○ 공동건축에 대하여는 지구단위계획결정도 참조
		형태	○ 건축물의 전후면과 측면은 동일계통의 재료, 색채 사용 ○ 옥상부분은 냉각탑 등 건축설비가 노출되지 않도록 함
		색채	○ 주조색 : 10YR ~ 2.5GY 8.5이상/2이하, N8 이상 ○ 보조색 : 2.5B ~ 10B 6.5~7.5/2~4 ○ 강조색 : 2.5B ~ 10B 3~5/4~7
		건축선	○ 건축지정선 - 광2-13호선 : 제1호건축선 (9m, 도로후퇴부분 6m) ○ 건축한계선 - 대1-36호선 : 제1호건축선 (9m, 도로후퇴부분 6m) - 15m, 10m 도로변 : 제3호건축선 (3m) - 완충녹지변 : 제4호건축선 (6m) - 보행자전용도로변 : 제6호건축선 (1m)

➡ 사유 : 토지분할 및 투자유치 협약에 따른 건축물의 용도 변경

도면 번호	위치	구분	계 획 내 용
	Ia-4, Ia-5, Ia-6	용도	▸ Ia-4(1,2,5,6), Ia-6(1) ○ 지정용도 - 주용도 : 연면적(주차장 및 기계실 등 제외)의 60% 이상 • 업무시설 - 부용도 : 연면적(주차장 및 기계실 등 제외)의 40% 이하 • 제1종근린생활시설 (‘가’목, ‘나’목, ‘다’목, ‘라’목에 한하며, ‘라’목 중 안마원 제외) • 제2종근린생활시설 (‘나’목 종교집회장, ‘마’목 총포판매소, ‘차’목 중 장의사, ‘파’목 중 옥외 골프연습장, ‘거’목 다중생활시설, ‘더’목 단란주점, ‘러’목 안마시술소, 노래연습장 제외) • 문화 및 집회시설(‘라’목 전시장) • 교육연구시설(‘라’목 학원, ‘마’목 연구소) • 노유자시설(‘가’목 아동 관련 시설) ○ 불허용도 - 지정용도 이외의 용도 ▸ Ia-4(3,4,7,8), Ia-5, Ia-6(2) ○ 지정용도 - 주용도 : 연면적(주차장 및 기계실 등 제외)의 80% 이상 • 업무시설(오피스텔 제외) - 부용도 : 연면적(주차장 및 기계실 등 제외)의 20% 이하 • 제1종근린생활시설 (‘가’목, ‘나’목, ‘다’목, ‘라’목에 한하며, ‘라’목 중 안마원 제외) • 제2종근린생활시설 (‘나’목 종교집회장, ‘마’목 총포판매소, ‘차’목 중 장의사, ‘파’목 중 옥외 골프연습장, ‘거’목 다중생활시설, ‘더’목 단란주점, ‘러’목 안마시술소, 노래연습장 제외) • 문화 및 집회시설(‘라’목 전시장) • 교육연구시설(‘라’목 학원, ‘마’목 연구소) • 노유자시설(‘가’목 아동 관련 시설) ○ 불허용도 - 지정용도 이외의 용도 ▸ Ia-6(3) ○ 지정용도 - 주용도 : 연면적(주차장 및 기계실 등 제외)의 80% 이상 • 업무시설(오피스텔 제외) • 교육연구시설(‘나’목 교육원, ‘다’목 직업훈련소, ‘마’목 연구소) - 부용도 : 연면적(주차장 및 기계실 등 제외)의 20% 이하 • 제1종근린생활시설 (‘가’목, ‘나’목, ‘다’목, ‘라’목에 한하며, ‘라’목 중 안마원 제외) • 제2종근린생활시설 (‘나’목 종교집회장, ‘마’목 총포판매소, ‘차’목 중 장의사, ‘파’목 중 옥외 골프연습장, ‘거’목 다중생활시설, ‘더’목 단란주점, ‘러’목 안마시술소, 노래연습장 제외) • 문화 및 집회시설(‘라’목 전시장) • 노유자시설(‘가’목 아동 관련 시설) ○ 불허용도 - 지정용도 이외의 용도

도면 번호	위치	구분	계 획 내 용
	Ia-4, Ia-5, Ia-6	건폐율	○ 50%이하
		용적률	○ 200%이하
		높이	○ 건축허가 이전에 인천경제자유구역청 경관위원회(심의)를 통해서 결정
		배치	○ 건축물의 벽면은 도로(보행자전용도로 제외)변과 평행 ○ 공동건축에 대하여는 지구단위계획결정도 참조
		형태	○ 건축물의 전후면과 측면은 동일계통의 재료, 색채 사용 ○ 옥상부분은 냉각탑 등 건축설비가 노출되지 않도록 함
		색채	○ 주조색 : 10YR ~ 2.5GY 8.5이상/2이하, N8 이상 ○ 보조색 : 2.5B ~ 10B 6.5~7.5/2~4 ○ 강조색 : 2.5B ~ 10B 3~5/4~7
		건축선	○ 건축한계선 - 대2-62호선, 대1-36호선변 : 제2호건축선 (6m, 도로후퇴부분3m) - 대3-74호선, 15m 도로변 : 제3호건축선 (3m)

도면 번호	위치	구분	계 획 내 용
	Ia-9	용도	► Ia-9(1) ○ 지정용도 - 주용도 : 연면적(주차장 및 기계실 등 제외)의 40% 이상 • 업무시설 (오피스텔 제외) - 부용도 : 연면적(주차장 및 기계실 등 제외)의 60% 이하 (단, 오피스텔 40%이하, 오피스텔 이외의 부용도 20%이하) • 제1종근린생활시설(‘가’목, ‘나’목, ‘다’목, ‘라’목에 한하며, ‘라’목 중 안마원 제외) • 제2종근린생활시설 (‘나’목 종교집회장, ‘마’목 총포판매소, ‘차’목 중 장의사, ‘파’목 중 옥외골프연습장, ‘거’목 다중생활시설, ‘더’목 단란주점, ‘러’목 안마시술소, 노래연습장 제외) • 문화 및 집회시설(‘가’목 공연장) • 판매시설 • 교육연구시설(‘라’목 학원, ‘마’목 연구소) • 업무시설(오피스텔에 한함) ○ 불허용도 - 지정용도 이외의 용도 ► Ia-9(3) ○ 지정용도 - 주용도 : 연면적(주차장 및 기계실 등 제외)의 80% 이상 • 업무시설 (오피스텔 제외) - 부용도 : 연면적(주차장 및 기계실 등 제외)의 20% 이하 • 제1종근린생활시설(‘가’목, ‘나’목, ‘다’목, ‘라’목에 한하며, ‘라’목 중 안마원 제외) • 제2종근린생활시설 (‘나’목 종교집회장, ‘마’목 총포판매소, ‘차’목 중 장의사, ‘파’목 중 옥외골프연습장, ‘거’목 다중생활시설, ‘더’목 단란주점, ‘러’목 안마시술소, 노래연습장 제외) • 문화 및 집회시설(‘가’목 공연장) • 판매시설 • 교육연구시설(‘라’목 학원, ‘마’목 연구소) ○ 불허용도 - 지정용도 이외의 용도
		건폐율	○ 50%이하
		용적률	○ 300%이하
		높이	○ 건축허가 이전에 인천경제자유구역청 경관위원회(심의)를 통해서 결정
		배치	○ 건축물의 벽면은 도로(보행자전용도로 제외)변과 평행 ○ 공동건축에 대하여는 지구단위계획결정도 참조
		형태	○ 건축물의 전후면과 측면은 동일계통의 재료, 색채 사용 ○ 옥상부분은 냉각탑 등 건축설비가 노출되지 않도록 함
		색채	○ 주조색 : 10YR ~ 2.5GY 8.5이상/2이하, N8 이상 ○ 보조색 : 2.5B ~ 10B 6.5~7.5/2~4 ○ 강조색 : 2.5B ~ 10B 3~5/4~7
		건축선	○ 건축지정선 - 광2-13호선 : 제1호건축선 (9m, 도로후퇴부분 6m) ○ 건축한계선 - 대3-74호선, 15m, 10m 도로변 : 제3호건축선 (3m) - 보행자전용도로변 : 제6호건축선 (1m)

(7) 지식기반R&D용지(변경없음)

(8) 지식기반제조업용지(변경없음)

(9) 교육시설용지(변경없음)

(10) 공공업무용지(변경없음)

(11) 폐기물처리시설용지(변경없음)

(12) 주차장용지(변경없음)

2) 테크노파크 부문(변경)

(1) 관련기업용지(변경)

▨ 관련기업용지(Ta-1(3~7), Tb-1, Tb-2, Tb-3)

도면번호	위 치	구분		계 획 내 용
	Ta-1(3~7) Tb-1 Tb-2 Tb-3	용도	기정	○ 지정용도 - 교육연구시설(연구소에 한하되, “산업기술단지지원에관한특례법” 제9조 및 동법시행령 제6조 제1항 제1호, 제4호, 제6호에 해당하는 건물 및 시설) - 유치업종 : 전자・정보, 신소재, 메카트로닉스/정밀기기, 생물 ○ 불허용도 : 지정용도 이외의 용도
			변경	○ 지정용도 - 교육연구 및 복지시설(연구소에 한하되, 아래에 해당하는 건물 및 시설) ・“산업기술단지지원에관한특례법” 제2조제1호 각 목의 사업을 수행하기 위하여 필요한 기업의 건물 및 시설(공동연구개발, 연구개발시설의 공동이용, 시험생산, 기타 기술의 실용화를 위하여 중소벤처기업부령이 정하는 시설) ・“벤처기업육성에 관한 특별조치법” 제2조제4항에 및 동법시행령 제2조, “중소기업창업지원법” 제2조 및 동법시행령 제2조의 규정에 의한 벤처기업 및 이에 준하는 R&D형 기업이 연구, 개발, 시험생산 등의 사업을 수행하기 위하여 필요한 건물 및 시설 ・“기초연구진흥 및 기술개발지원에 관한 법률” 제14조제1항 제2호에 따른 기업부설연구소가 수행하는 사업에 필요한 건물 및 시설 ※ 유치업종 : 전자・정보, 신소재, 메카트로닉스/정밀기기, 생물 ○ 불허용도 : 지정용도 이외의 용도

도면번호	위 치	구분	계 획 내 용
	Ta-1(3~7) Tb-1 Tb-2 Tb-3	건폐율	○60%이하
		용적률	○200%이하
		높이	○5층이하
		배치	○건축물의 벽면은 도로변과 평행하도록 할 것 ○건축한계선 : 전지역 5m
		형태	○건축물의 모든 외벽은 전면과 측면의 구별 없이 모든면의 마감을 동일한 수준으로 처리 ○외벽의 마감재료중 샌드위치단열판넬 등의 가설조립식판넬은 사용할 수 없으며, 유사외장재를 사용할 경우에는 색상, 규격, 재질 등을 단지관리기관의 승인을 받은 후 사용하여야 한다. ○어린이 공원을 축으로 지나는 보행자도로에 면한 1층 외벽면의 50% 이상은 투시벽 설치(권장) ○옥상부분은 냉각탑 등 건축설비가 노출되지 않도록 할 것 ○셔터를 설치할 경우 투시형 셔터를 설치 ○지붕재료는 반사되지 않는 재료를 사용하며, 건물 내부 이용자들을 위한 옥상정원 설치 (권장) ○단기간의 존치를 목적으로 한 가설 건축물 등의 구조체는 건축할 수 없음
		색채	○주조/보조색 : 2.5B ~ 10B 8이상/2이하, N8 이상 ○강조색 : 5BG~10B5~7/4~7

➡ 사유 : 「산업기술단지지원에관한특례법」 시행령 제6조 개정내용(규제방식 변경: 포지티브→네거티브) 반영

(2) R&D용지(변경)

▨ R&D용지(Ta-1(1), Ta-2, Ta-3)

도면번호	위 치	구분		계 획 내 용
	Ta-1(1) Ta-2(1) Ta-3	용도	기정	① Ta-1(1), Ta-2(1), Ta-3 ○ 지정용도 - 교육연구 및 복지시설(학교, 연구소에 한함), - 업무시설로서 “산업기술단지지원에관한특례법” 제9조 및 동법 시행령 제6조 제1항 제1호, 제2호, 제3호, 제4호, 제5호, 제7호, 제8호에 해당 하는 건물 및 시설 ○ 불허용도 : 지정용도 이외의 용도
			변경	○ 지정용도 - 교육연구 및 복지시설(학교, 연구소에 한함) - 업무시설(아래에 해당하는 건물 및 시설, 오피스텔 제외) · “산업기술단지지원에관한특례법” 제2조제1호 각 목의 사업을 수행하기 위하여 필요한 기업의 건물 및 시설(공동연구개발, 기술인력의 교육 및 훈련, 산업 및 기술에 관한 정보의 유통, 신기술 보육 및 창업, 연구개발시설의 공동이용, 시험생산 기타 기술의 실용화를 위하여 중소벤처기업부령이 정하는 사업 · “고등교육법” 제2조에 따른 학교 · “산업기술연구조합 육성법”에 따른 산업기술연구조합이 수행하는 사업에 필요한 건물 및 시설 · “벤처기업 육성에 관한 특별 조치법” 제2조제4항에 따른 벤처기업 집적시설 · “특정연구기관 육성법 시행령” 제3조에 따른 연구기관이 수행하는 사업에 필요한 건물 및 시설 · “과학기술분야 정부출연연구기관 등의 설립, 운영 및 육성에 관한법률” 제8조의 규정에 의한 연구기관이 수행하는 사업에 필요한 건물 및 시설 · 국공립 연구기관이 수행하는 사업에 필요한 건물 및 시설 · 바이오 기술을 제품화하기 위하여 설치하는 생물산업기술 실용화센터 · “민법” 또는 다른 법률에 따라 설립된 비영리 법인이 수행하는 사업에 필요한 건물 및 시설 ○ 불허용도 : 지정용도 이외의 용도

도면번호	위 치	구분	계 획 내 용	
	Ta-1(1) Ta-2(1) Ta-3	건폐율	Ta-1(1), Ta-2, Ta-3(1,2,4)	40%이하
			Ta-3(3)	60%이하
		용적률	Ta-2, Ta-3(1,2,4)	100%이하
			Ta-1(1)	150%이하
			Ta-3(3)	200%이하
		높이	Ta-2, Ta-3	5층이하
			Ta-1(1)	21층이하
		배치	○ 건축물의 벽면은 도로변과 평행하도록 할 것 ○ 건축한계선 : 전지역 5m	
		형태	○ 건축물의 모든 외벽은 전면과 측면의 구별없이 모든면의 마감을 동일한 수준으로 처리 ○ 외벽의 마감재료중 샌드위치 단열판넬 등의 가설조립식판넬은 사용할 수 없으며, 유사외장재를 사용할 경우에는 색상, 규격, 재질 등을 단지관리기관의 승인을 받은 후 사용하여야 한다. ○ 옥상부분은 냉각탑 등 건축설비가 노출되지 않도록 할 것 ○ 셔터를 설치할 경우 투시형 셔터를 설치 (권장) ○ 지붕재료는 반사되지 않는 재료를 사용하며, 건물내부 이용자들을 위한 옥상정원 설치 (권장) ○ 단기간의 존치를 목적으로 한 가설 건축물 등의 구조체는 건축할 수 없음	
		색채	○ 주조/보조색 : 2.5B ~ 10B 8이상/2이하, N8 이상 ○ 강조색 : 5BG~10B5~7/4~7	

도면번호	위 치	구분		계 획 내 용
	Ta-2(2)	용도	기정	② Ta-2(2) ○ 지정용도 - 교육연구 및 복지시설(학교, 연구소에 한함), 업무시설로서 산업기술단지지원에관한특례법” 제9조 및 동법시행령 제6조 제1항 제1호, 제2호, 제3호, 제4호, 제5호, 제7호, 제8호에 해당하는 건물 및 시설 - 건축법시행령 별표1 제17호의 공장으로서의 시설 ○ 불허용도 : 지정용도 이외의 용도
			변경	○ 지정용도 - 교육연구 및 복지시설(학교, 연구소에 한함) - 업무시설(아래에 해당하는 건물 및 시설, 오피스텔 제외) · “산업기술단지지원에관한특례법” 제2조제1호 각 목의 사업을 수행하기 위하여 필요한 기업의 건물 및 시설 · “고등교육법” 제2조에 따른 학교 · “산업기술연구조합 육성법”에 따른 산업기술연구조합이 수행하는 사업에 필요한 건물 및 시설 · “벤처기업육성에 관한 특별조치법” 제2조제4항에 따른 벤처기업 집적시설 · “특정연구기관 육성법시행령” 제3조에 따른 연구기관이 수행하는 사업에 필요한 건물 및 시설 · 국공립 연구기관이 수행하는 사업에 필요한 건물 및 시설 · “민법” 또는 다른 법률에 따라 설립된 비영리 법인이 수행하는 사업에 필요한 건물 및 시설 - 건축법시행령 별표1 제17호의 공장으로서의 시설 ○ 불허용도 : 지정용도 이외의 용도
		건폐율		40%이하
		용적률		100%이하
		높이		5층이하

도면번호	위 치	구분	계 획 내 용
	Ta-2(2)	배치	○건축물의 벽면은 도로변과 평행하도록 할 것 ○건축한계선 : 전지역 5m
		형태	○건축물의 모든 외벽은 전면과 측면의 구별없이 모든면의 마감을 동일한 수준으로 처리 ○외벽의 마감재료중 샌드위치단열판넬 등의 가설조립식 판넬은 사용할 수 없으며, 유사외장재를 사용할 경우에는 색상, 규격, 재질 등을 단지관리 기관의 승인을 받은 후 사용하여야 한다. ○옥상부분은 냉각탑 등 건축설비가 노출되지 않도록 할 것 ○셔터를 설치할 경우 투시형 셔터를 설치 (권장) ○지붕재료는 반사되지 않는 재료를 사용하며, 건물내부 이용자들을 위한 옥상정원 설치 (권장) ○단기간의 존치를 목적으로 한 가설 건축물 등의 구조체는 건축할 수 없음
		색채	○주조/보조색 : 2.5B ~ 10B 8이상/2이하, N8 이상 ○강조색 : 5BG~10B5~7/4~7

➡ 사유 : 「산업기술단지지원에관한특례법」 시행령 제6조 개정내용(규제방식 변경: 포지티브→네거티브) 반영

(3) 교육시설용지(변경)

▨ 교육시설용지(대2, 대3)

도면번호	위 치	구분		계 획 내 용
	대2 대3	용도	기정	◦ 지정용도 - 교육연구 및 복지시설 (학교, 연구소에 한함) - 업무시설로서 “산업기술단지지원에관한특례법” 제9조 및 동법시행령 제6조 제1항 제1호, 제2호, 제3호, 제4호, 제5호, 제7호, 제8호에 해당하는 건물 및 시설 ◦ 불허용도 : 지정용도 이외의 용도
			변경	○ 지정용도 - 교육연구시설(학교, 연구소에 한함) - 업무시설(아래에 해당하는 건물 및 시설, 오피스텔 제외) ·“산업기술단지지원에관한특례법” 제2조제1호 각 목의 사업을 수행하기 위하여 필요한 기업의 건물 및 시설 ·“고등교육법” 제2조에 따른 학교 ·“산업기술연구조합육성법”에 따른 산업기술 연구조합이 수행하는 사업에 필요한 건물 및 시설 ·“벤처기업육성에 관한 특별조치법” 제2조제4항에 따른 벤처기업 집적시설 ·“특정연구기관 육성법 시행령” 제3조에 따른 연구기관이 수행하는 사업에 필요한 건물 및 시설 ·국공립 연구기관이 수행하는 사업에 필요한 건물 및 시설 ·“민법” 또는 다른 법률에 따라 설립된 비영리 법인이 수행하는 사업에 필요한 건물 및 시설 ○ 불허용도 : 지정용도 이외의 용도
		건폐율		40%이하
		용적률		100%이하
		높이		5층

➡ 사유 : 「산업기술단지지원에관한특례법」 시행령 제6조 개정내용(규제방식 변경: 포지티브→네거티브) 반영

라. 기타사항에 관한 도시관리계획 결정조서(변경)


1) 테크노벨리 부문(변경없음)

2) 테크노파크 부문(변경없음)

3) 기타사항(변경)

▨ 교통처리계획 (변경)

지구단위계획결정(변경)도
-건축물의용도·건폐율·용적률·높이·배치·형태·색채·건축선에 관한 계획-

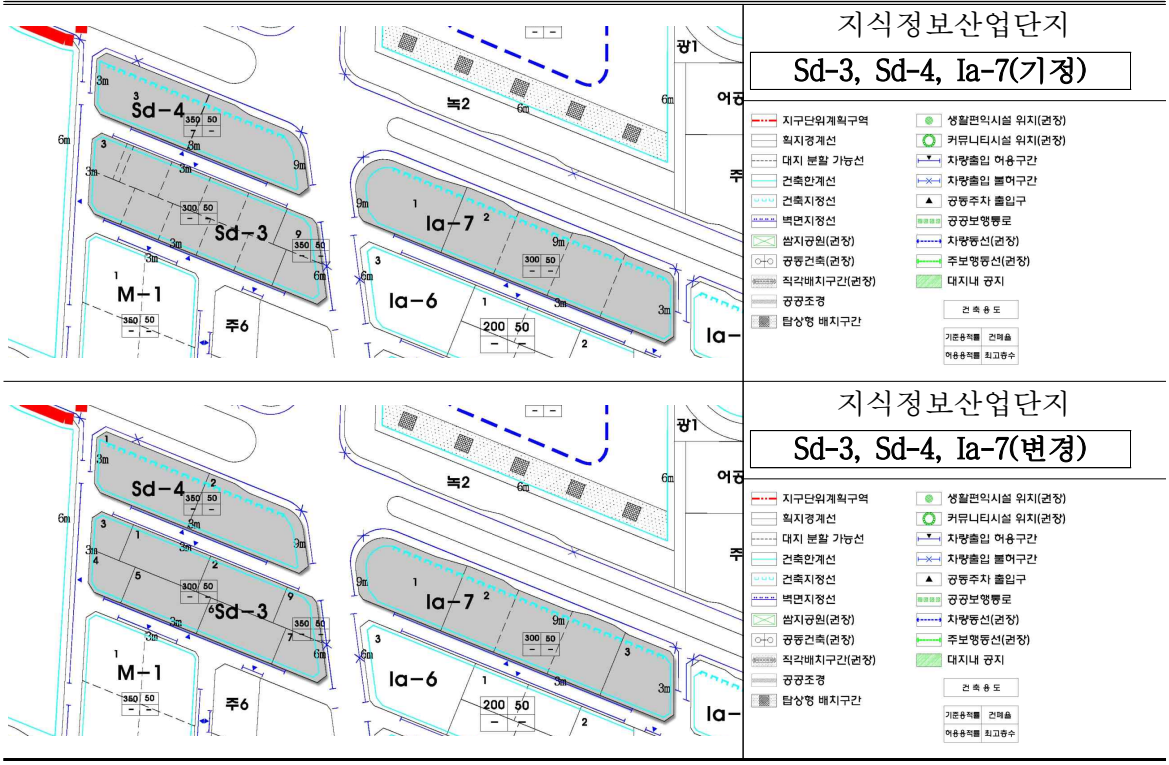

➡ 사유 : 토지 분할에 따른 Sd-3(9) 차량진출입 허용구간 변경

▨ 건축지정선의 설정 (추가)

○ 가로경관의 연속적인 형태를 유지하거나 가로변의 건물을 가지런하게 하기 위해 건축물의 외벽위치를 지정한 선

○ 건축물의 외벽면이 건축지정선 길이의 2/3이상에 해당하는 길이만큼 그 선의 수직면에 접하여야 함

구 분	규 제 내 용	규 제 적 용 범 위
건축지정선	1호건축선 : 9m 이상(도로의 후퇴부분 6m 이상)	광1-2호선변(Sd-4) 광2-13호선변(Ia-7, Ia-9, Ic-9)

➡ 사유 : 건축지정선에 관한 정의 누락에 따른 내용 추가

마. 지구단위계획 운용에 관한 계획(변경없음)